


NB. OVERALL SOLIDITY OF FENCE SYSTEM INCLUDING
DEBRIS NETTING TO BE TAKEN AS 40%

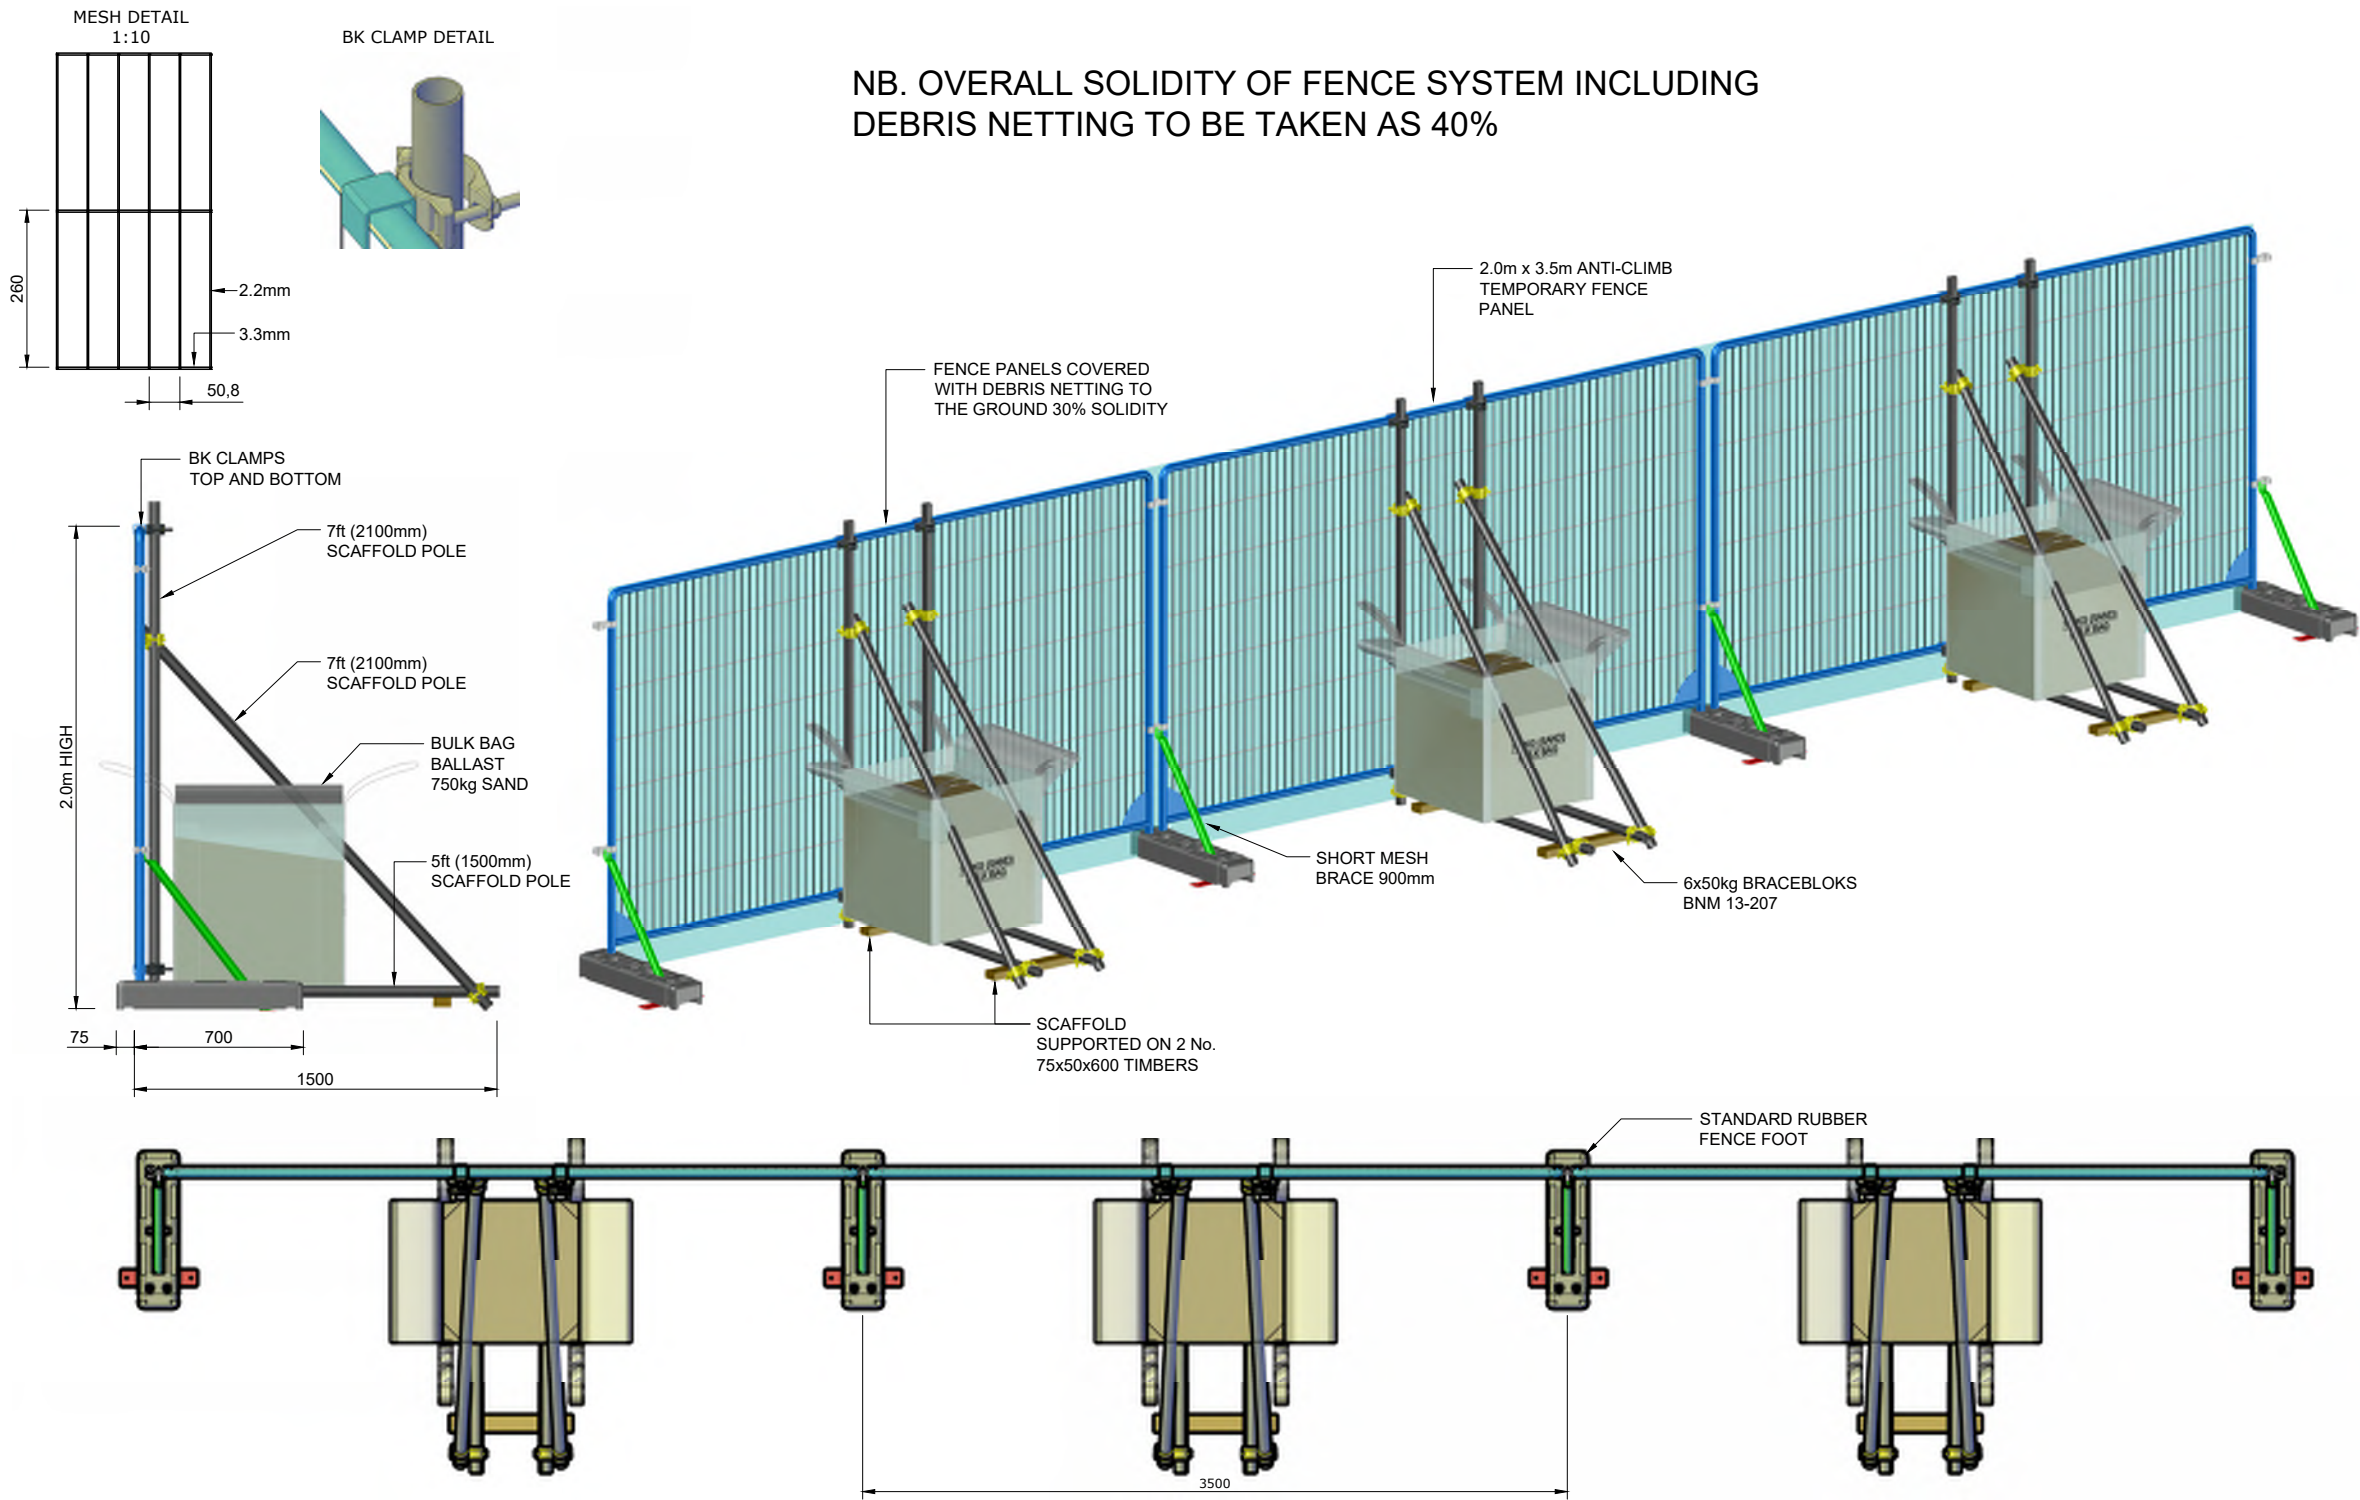

Prior to installing site are required to check all of the
following details are correct:

POSTCODE:

MAP:

Installation Month:

Installation Duration:

Distance to Sea, km:

Altitude,m:

Distance to Sea, km:

Terrain category (EN 1991-1-4):

Ground Conditions:

Design Wind Speed:

Design Wind Pressure:

Information input onto MWP standard design platform by:

REV	DATE	DESCRIPTION	BY	APP
CLIENT				
BROWNE				

MWP
ENGINEERING AND ENVIRONMENTAL CONSULTANTS
CORK | TRALEE | LONDON | LIMERICK
mwpeng.co.uk

PROJECT:
TITLE:

DRAWN:	CHECKED:	APPROVED:
PROJECT NUMBER:	DATE:	SCALE @ A3:
STATUS DESCRIPTION		STATUS:
DRAWING NUMBER:		REV: